PORTFOLIO

SELECT WORKS OF INTERNSHIP FROM


27-01-2023 TO 09-03-2023

PRASHAM DHOKE

AR19019


CONTENT

- GOYANKA RESIDENCE (HINGANGHAT)
  - COMPOUND WALL PLAN AND ELEVATION WORKING DRAWING , VIEW.
- JAYADE RESIDENCE (AMRAVATI)
  - BED DETAILS WORKING DRAWING,SIDE TABLE WORKING DRAWING,TV UNIT DETAIL,CEILING DETAIL.
- DR. THORAT RESIDENCE (NAGPUR)
  - STAIRCASE WITH STRUCTURAL DETAILS, GROUND FLOOR BRICKWORK DETAIL.
- DAHAKE HOSPITAL (AMRAVATI)
  - PRESENTAION DRAWING OF FIRST FLOOR AND SECOND FLOOR
- KABRA RESIDENCE (NAGPUR)
  - FIRST FLOOR SLEEVES DRAWING FOR SLAB
- RENDERS
  - MUNDHADA RESIDENCE.

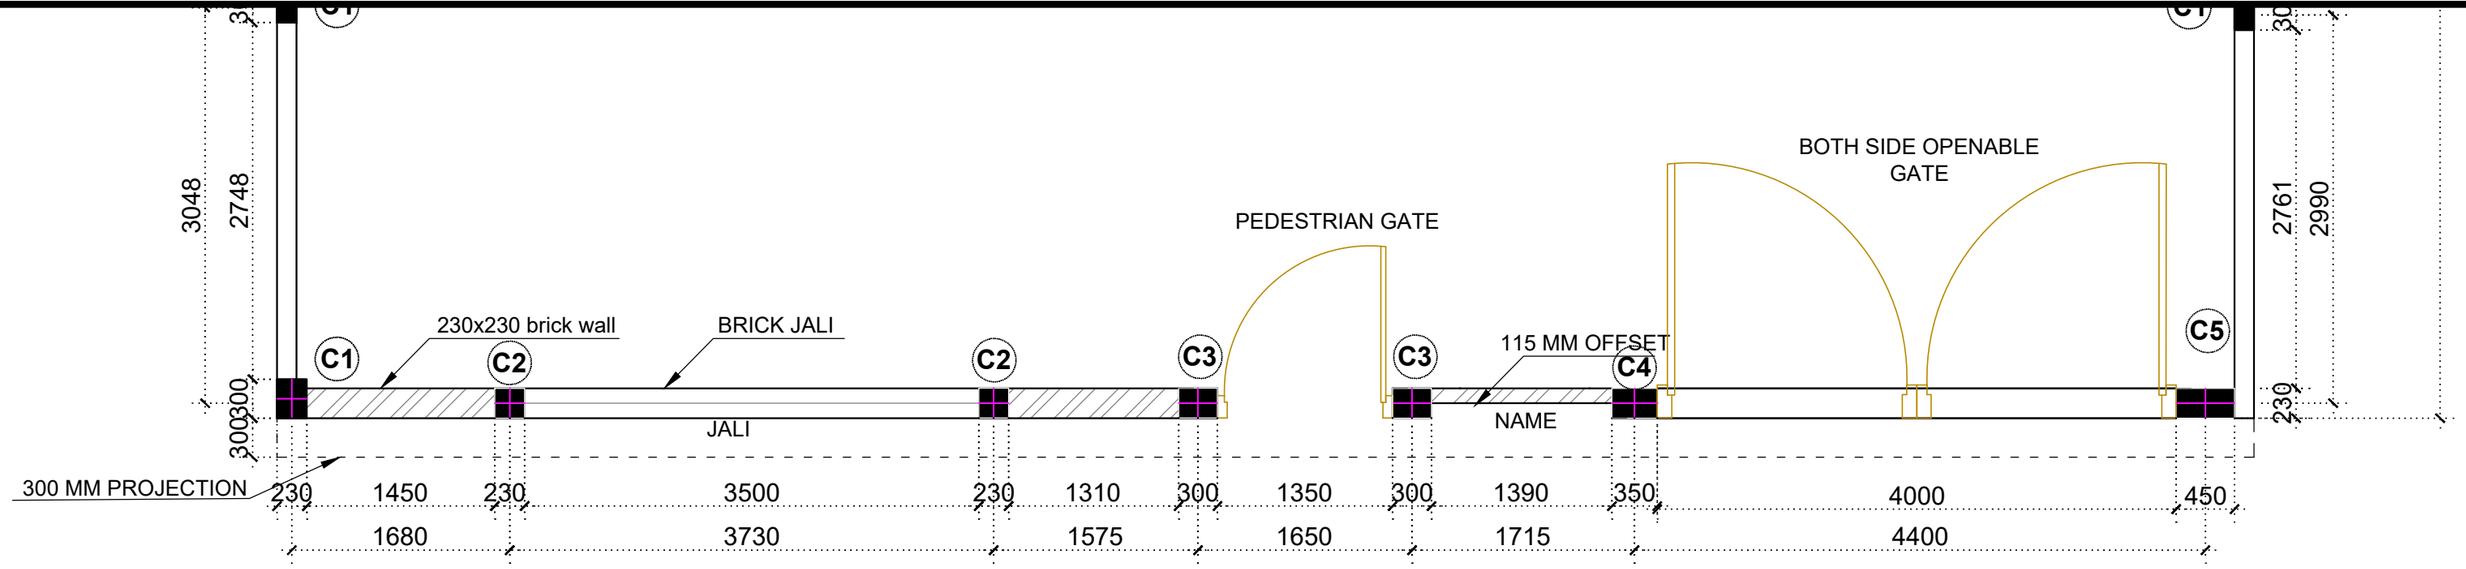

COMPOUND WALL PLAN

BRICK WORK LEVEL

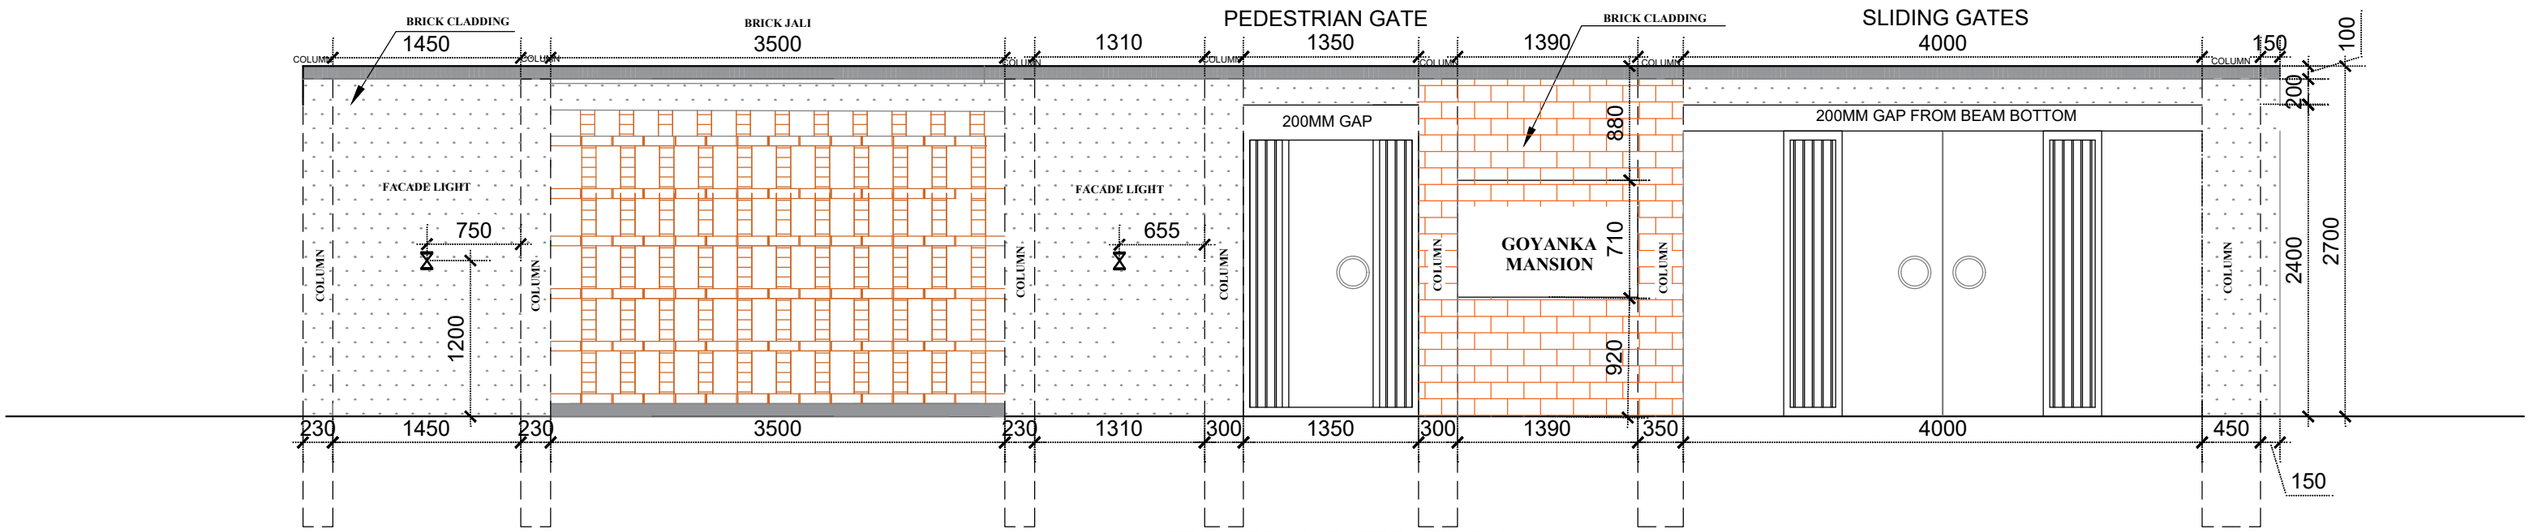

ELEVATION

STUDIO ADROIT ARCHITECTS

ARCHITECTS # PLANNERS # INTERIOR DESIGNERS

AR.VAIBHAV THAKRE & AR. PRAJAKT KARMARKAR

Parijat Apartment,Flat 403, Plot no.M5,
West High Court Road, Laxmi Nagar, Nagpur, Maharashtra 440022

E-mail: studioadroitarchitects@gmail.com, ar.vaibhav.thakre@gmail.com Phone: 9167356380, 8552006111

SHEET TITLE

COMPOUND WALL DETAILS

PROJECT NO

DRAWING NO

BELONGS TO-

MR. GOYANKA

DATE - 21 02 2023

DRAWN BY: PD CHECKED VT

REVISIONS

REV 1

REV 2

S E W N

SCALE N.T.S



STUDIO ADROIT ARCHITECTS

ARCHITECTS # PLANNERS # INTERIOR DESIGNERS

AR.VAIBHAV THAKRE & AR. PRAJAKT KARMARKAR

Parijat Apartment,Flat 403, Plot no.M5,
West High Court Road, Laxmi Nagar, Nagpur, Maharashtra 440022

E-mail: studioadroitarchitects@gmail.com, ar.vaibhav.thakre@gmail.com Phone: 9167356380, 8552006111

SHEET TITLE

COMPOUND WALL VIEW

BELONGS TO-

MR. GOYANKA

REVISIONS

REV 1

REV 2

PROJECT NO


DRAWING NO

DATE - 21 02 2023


DRAWN BY: PD CHECKED VT

S E W N


SCALE N.T.S

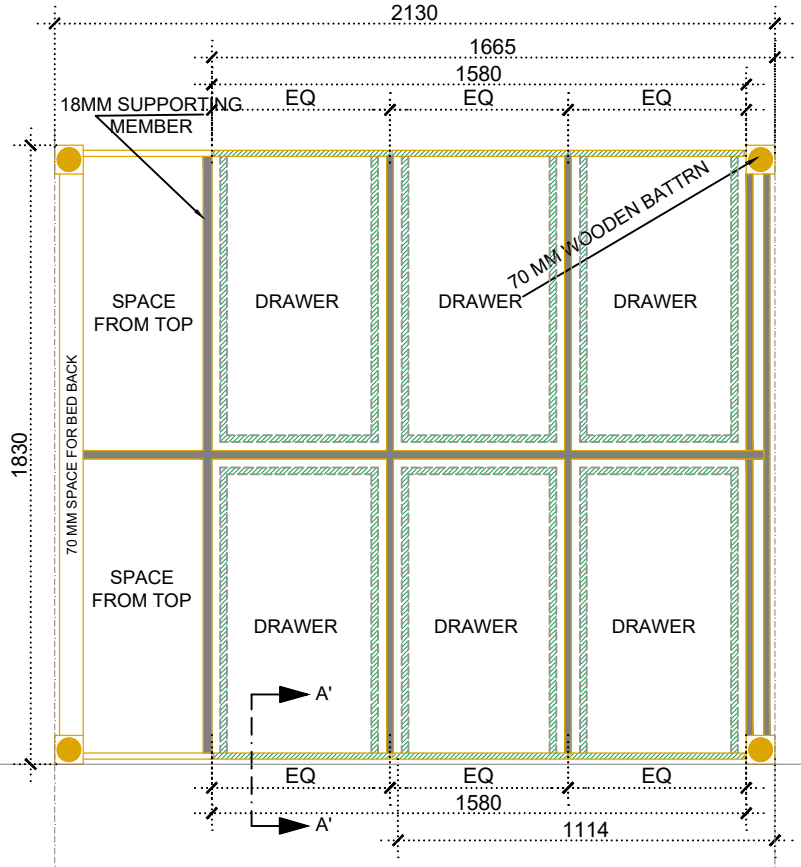


MASTER BEDROOM BED DRAWER PLAN

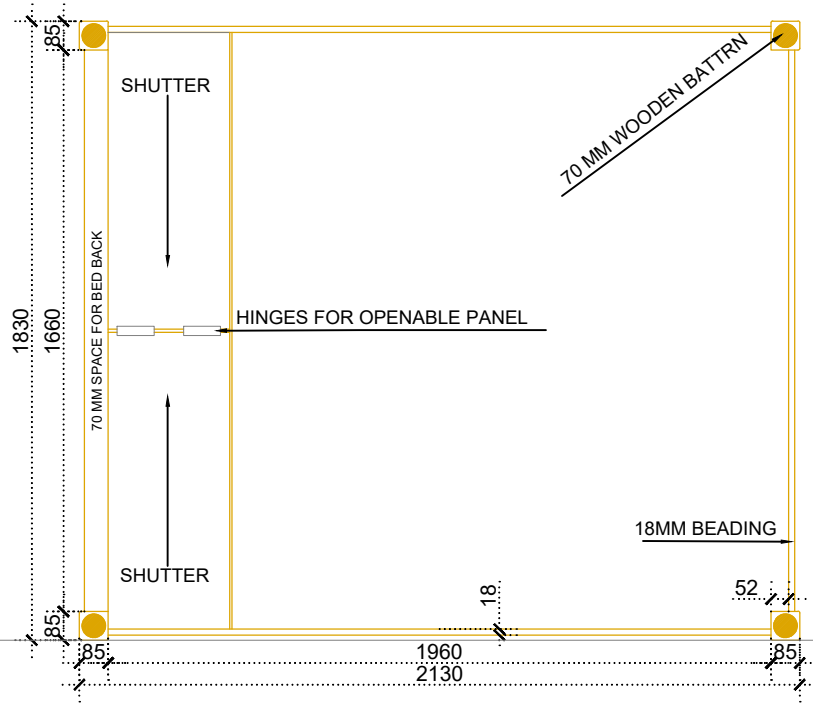


MASTER BEDROOM BED PLAN AT 350MM LVL

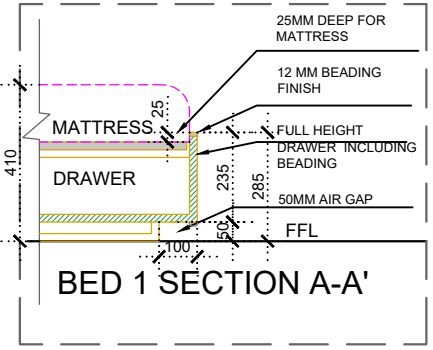


BED 1 SECTION A-A'

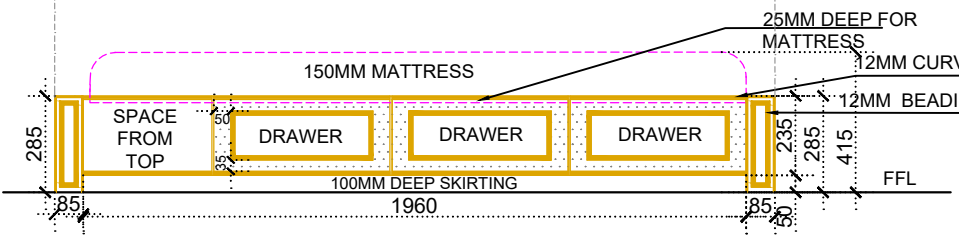

MASTER BEDROOM BED SIDE ELEVATION

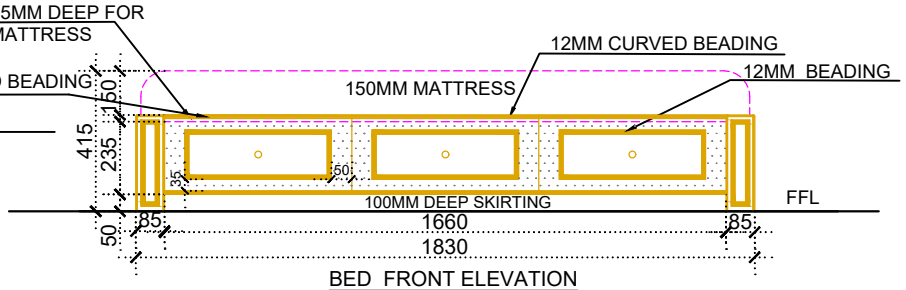

BED FRONT ELEVATION

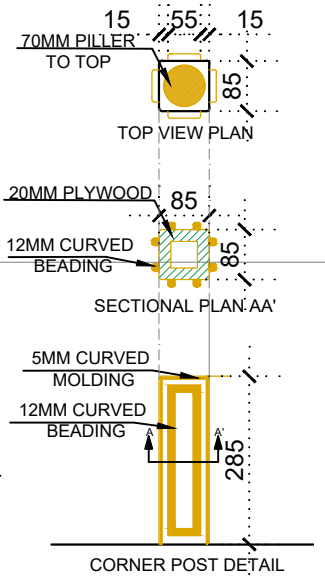

STUDIO ADROIT ARCHITECTS
ARCHITECTS # PLANNERS # INTERIOR DESIGNERS
AR.VAIBHAV THAKRE & AR. PRAJAKT KARMARKAR
Parijat Apartment,Flat 403, Plot no.M5,
West High Court Road, Laxmi Nagar, Nagpur, Maharashtra 440022
E-mail: studioadroitarchitects@gmail.com, ar.vaibhav.thakre@gmail.com Phone: 9167356380, 8552006111

SHEET TITLE
MASTER BED ROOM BED DETAILS

BELONGS TO-
JAYADE RESIDENCE

REVISIONS
REV 1
REV 2


PROJECT NO

DRAWING NO
1


DATE - 10 FEB 2023

DRAWN BY: PD CHECKED PK


SCALE N.T.S

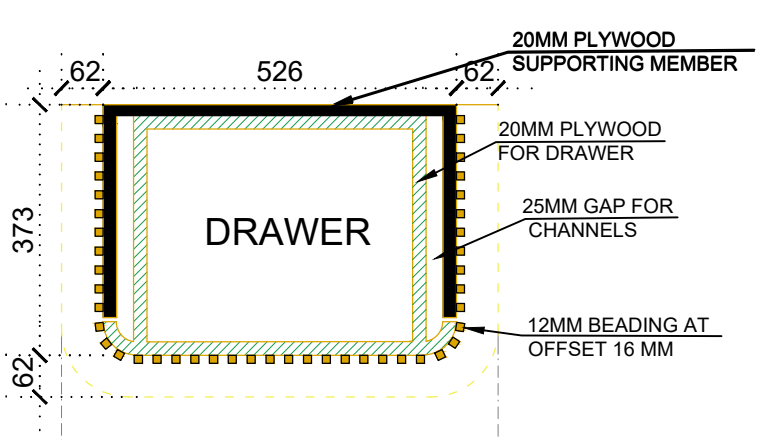


SIDE TABLE PLAN AT 150MM (AA')

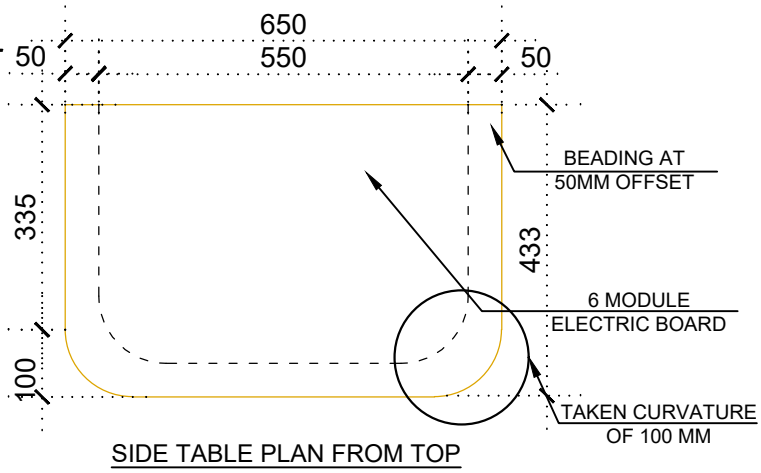

SIDE TABLE PLAN FROM TOP

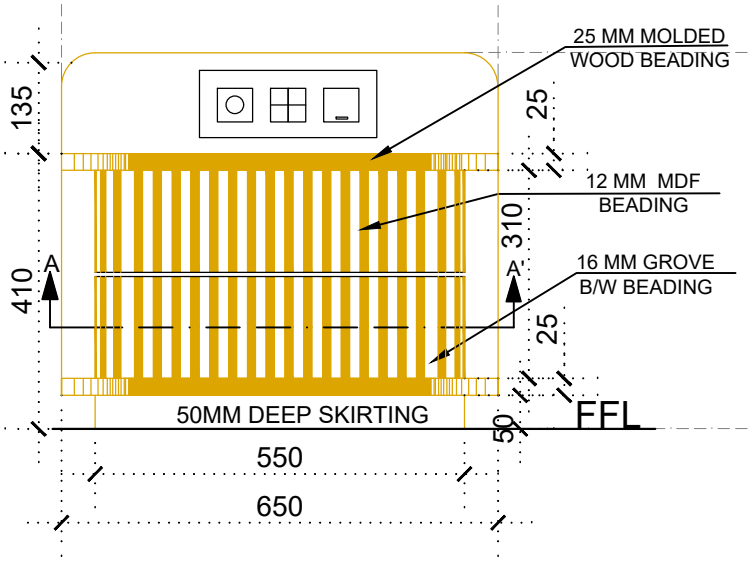

SIDE TABLE FRONT ELEVATION

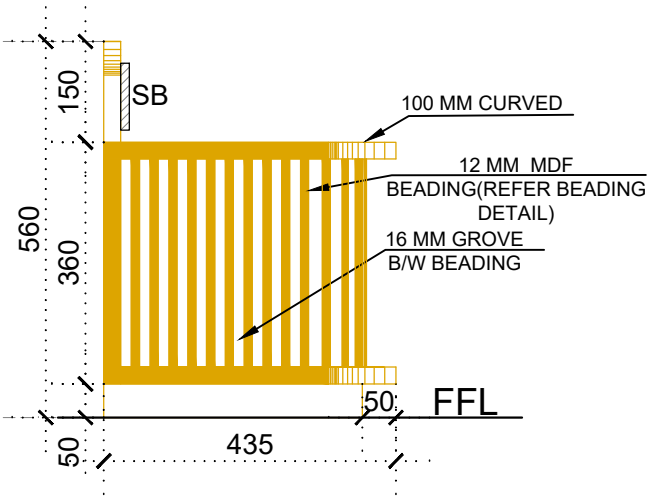


SIDE TABLE SIDE ELEVATION






STUDIO ADROIT ARCHITECTS # ARCHITECTS # PLANNERS # INTERIOR DESIGNERS # AR.VAIBHAV THAKRE & AR. PRAJAKT KARMARKAR Parijat Apartment,Flat 403, Plot no.M5, West High Court Road, Laxmi Nagar, Nagpur, Maharashtra 440022 E-mail: studioadroitarchitects@gmail.com, ar.vaibhav.thakre@gmail.com Phone: 9167356380, 8552006111	SHEET TITLE **MASTER BEDROOM SIDE TABLE DETAILS**	BELONGS TO- **JAYADE RESIDENCE**	REVISIONS REV 1 REV 2	
	PROJECT NO	DRAWING NO 1	DATE - 14 FEB 2023 DRAWN BY: PD CHECKED PK	SCALE N.T.S

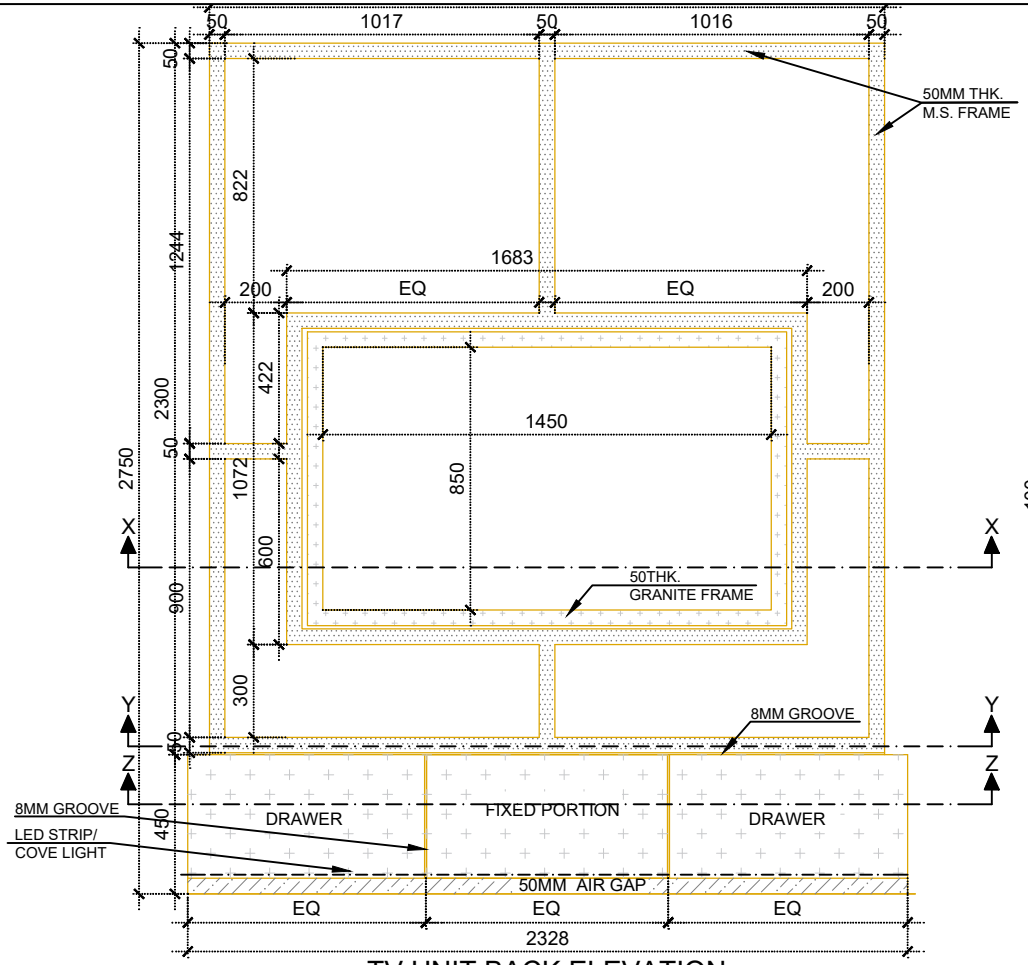


TV UNIT BACK ELEVATION

ELECTRICAL LAYOUT


SB.No	SYMBOL	DESCRIPTION	BOTTOM OF BOARD	REMARK	MODULE
7	5A	2 plug sockets for TV- 5 Amp with switch in 7A	1200 mm from ffl	On furniture paneling (point to be left in flooring)	6 Module plate Norisys
		1 CAT-6 / INTERNET socket (cat-6 directly from main internet modem @SB3A)			
		1 HDMI (from SB7B)			
7A		1 switch for TV (2 sockets @ SB7) ★	450 mm from ffl		6 Module plate Norisys (twin switch)
	5A	2 plug socket with 1 switch- 5 Amp			
7B		1 Cable point from building service duct	190 mm from ffl		6 Module plate
		1 HDMI from SB7			
		1 CAT-6 / INTERNET socket (for booster from @SB3A)			
	5A	2 plug socket with 1 switch- 5 Amp			

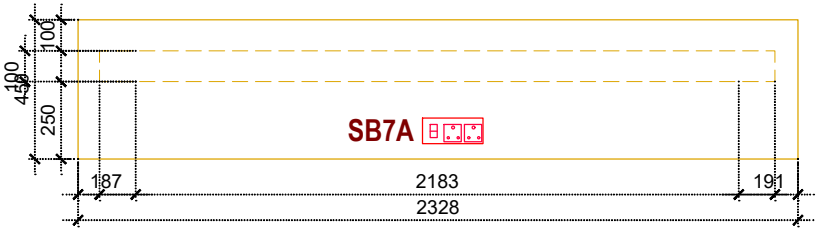


TV UNIT PLAN SECTION X-X'

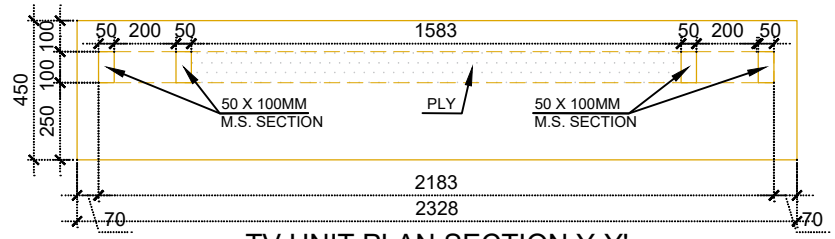


TV UNIT PLAN SECTION Y-Y'

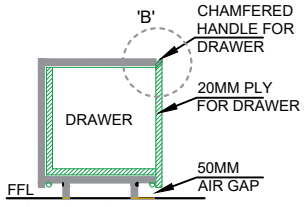

SECTION A-A'

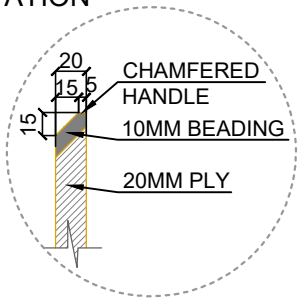

DETAIL AT 'B'

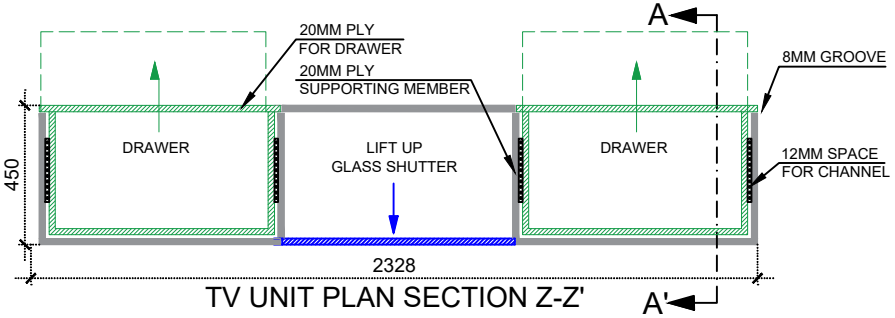

TV UNIT PLAN SECTION Z-Z'

STUDIO ADROIT ARCHITECTS

ARCHITECTS # PLANNERS # INTERIOR DESIGNERS

AR.VAIBHAV THAKRE & AR. PRAJAKT KARMARKAR

Parijat Apartment,Flat 403, Plot no.M5,
West High Court Road, Laxmi Nagar, Nagpur, Maharashtra 440022

E-mail: studioadroitarchitects@gmail.com, ar.vaibhav.thakre@gmail.com Phone: 9167356380, 8552006111

SHEET TITLE
TV UNIT

BELONGS TO-
JAYADE RESIDENCE

REVISIONS
REV 1
REV 2


PROJECT NO


DRAWING NO
2

DATE - 30 JAN 2023

DRAWN BY: AH CHECKED

SCALE N.T.S

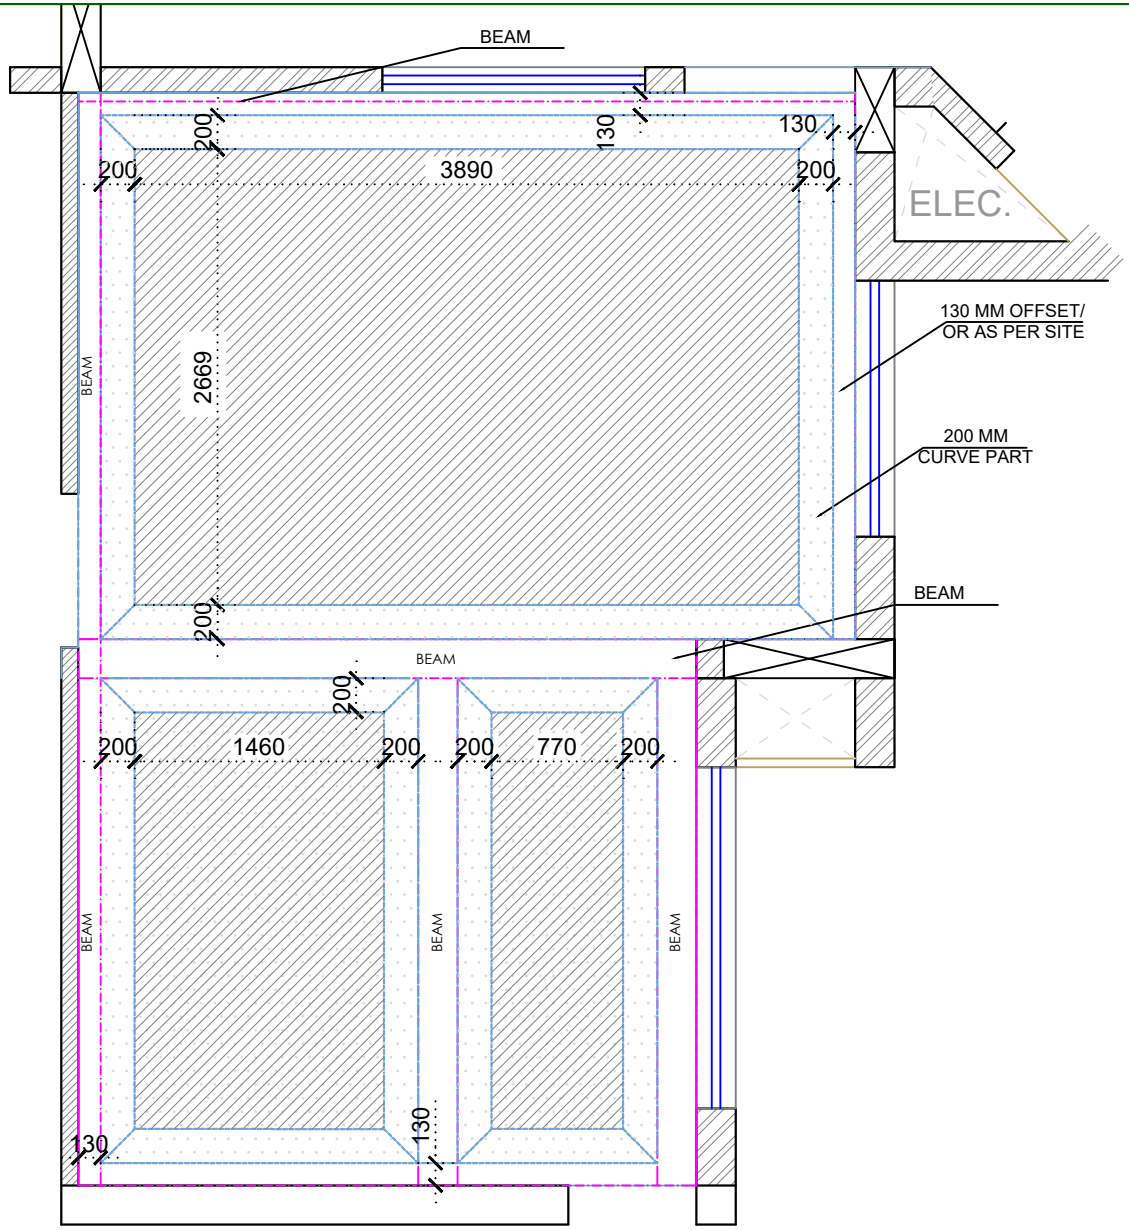

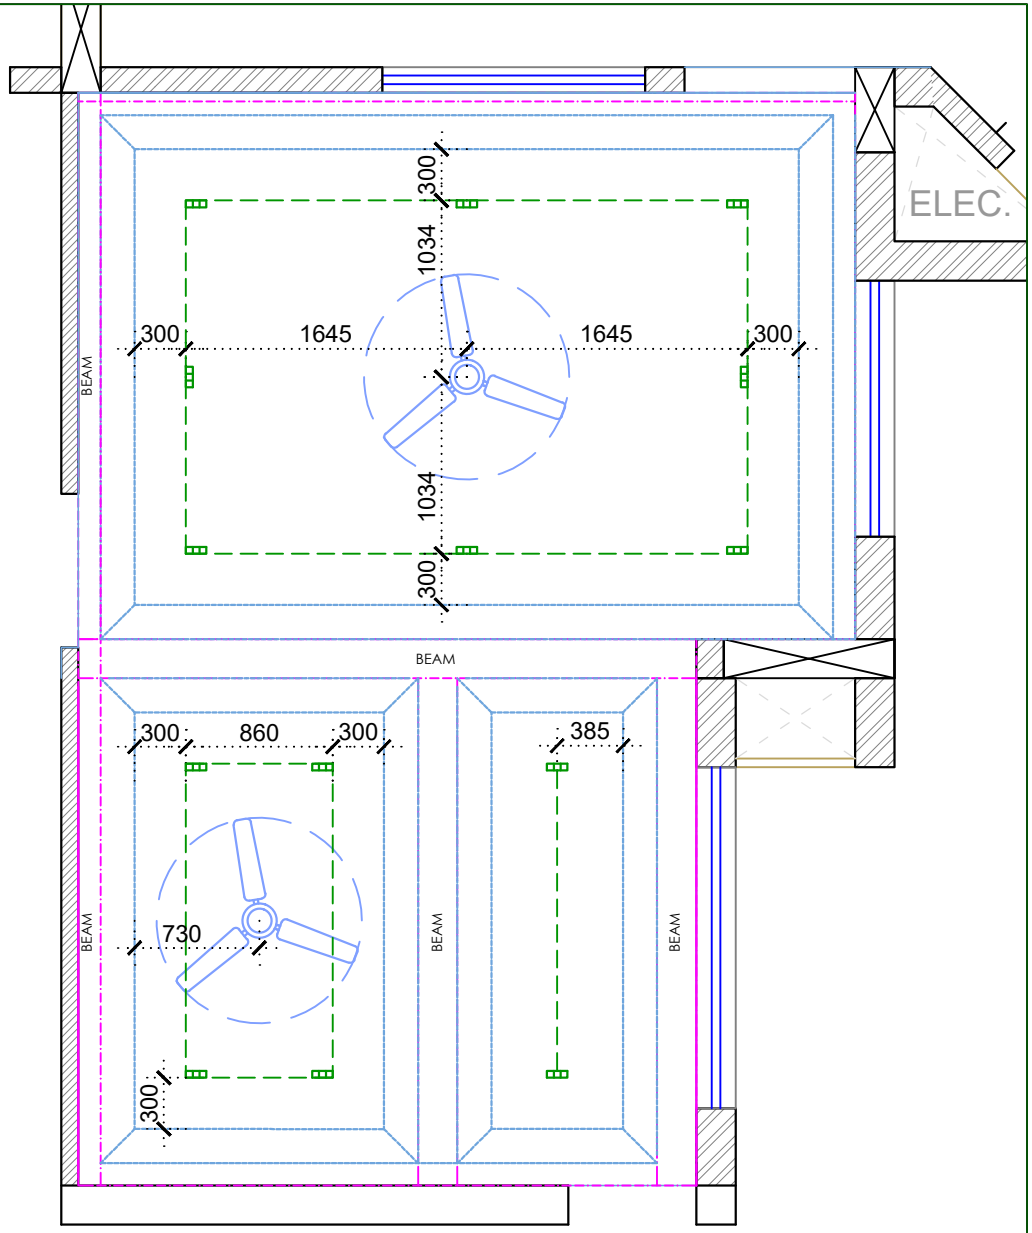

GUEST LIVING ROOM CEILING LAYOUT

CEILING ELECTRICAL LAYOUT

STUDIO ADROIT ARCHITECTS

ARCHITECTS # PLANNERS # INTERIOR DESIGNERS

AR.VAIBHAV THAKRE & AR. PRAJAKT KARMARKAR

Parijat Apartment,Flat 403, Plot no.M5,
West High Court Road, Laxmi Nagar, Nagpur, Maharashtra 440022

E-mail: studioadroitarchitects@gmail.com, ar.vaibhav.thakre@gmail.com Phone: 9167356380, 8552006111

SHEET TITLE

CEILING & ELECTRICAL LAYOUT

BELONGS TO-

JAYADE RESIDENCE

REVISIONS

REV 1

REV 2

PROJECT NO

DRAWING NO


DATE - 27 FEB 2023

DRAWN BY: PD CHECKED PK


SCALE N.T.S

SCHEDULE OF BEAMS AT PLINTH LEVEL


BEAM	SIZE B X D	BOTTOM STEEL			TOP STEEL		STIRRUPS c/c		REMARKS
		STRAIGHT	BOTTOM CURTAIL 2L/3 AT CENTRE	BENTUP BAR	STRAIGHT	EXTRA AT SUPPORT UPTO L/4	UPTO L/4	IN MIDDLE	
MB1	230x450	2x12 ϕ	2X12 ϕ	---ϕ	2X12 ϕ	2X12 ϕ	8 ϕ@ 100	8 ϕ @ 150	BEAM MIDLANDING
MBR	230x450	3X12 ϕ	---ϕ	---ϕ	6X12 ϕ	---ϕ	8 ϕ@ 100	8 ϕ @ 150	MIDLANDING CANTILEVER BEAM

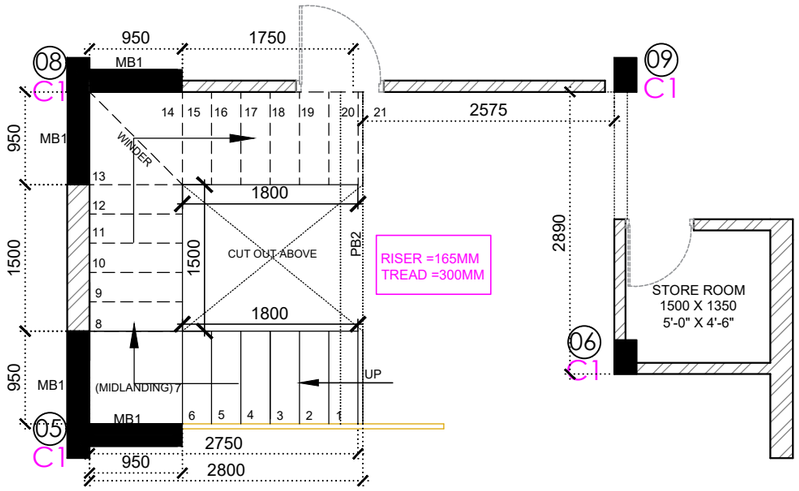



GROUND TO FIRST FLOOR STAIRCASE PLAN

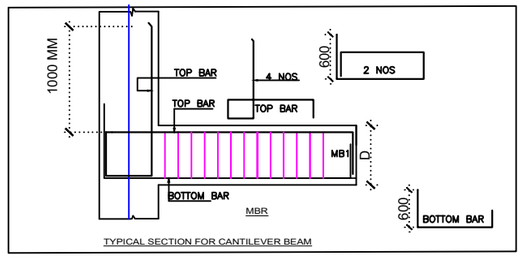

TYPICAL SECTION FOR CANTILEVER BEAM

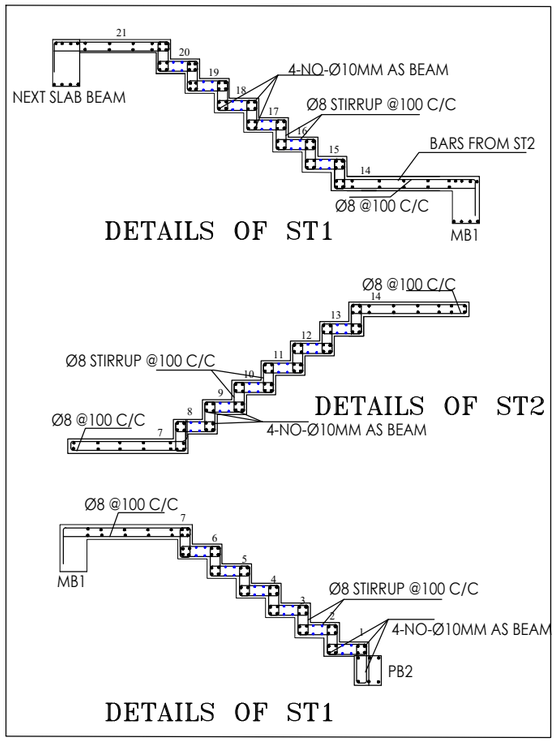

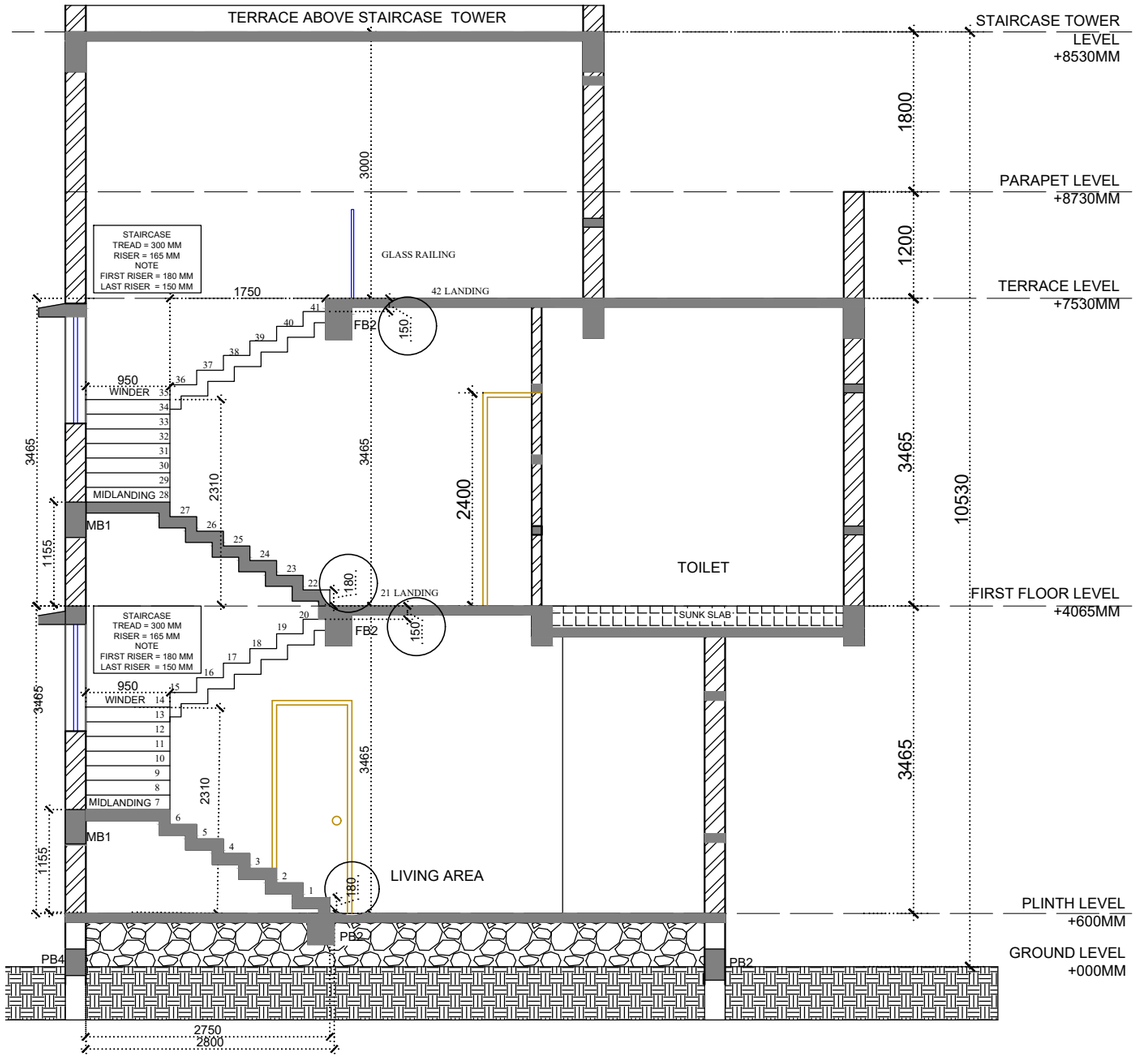

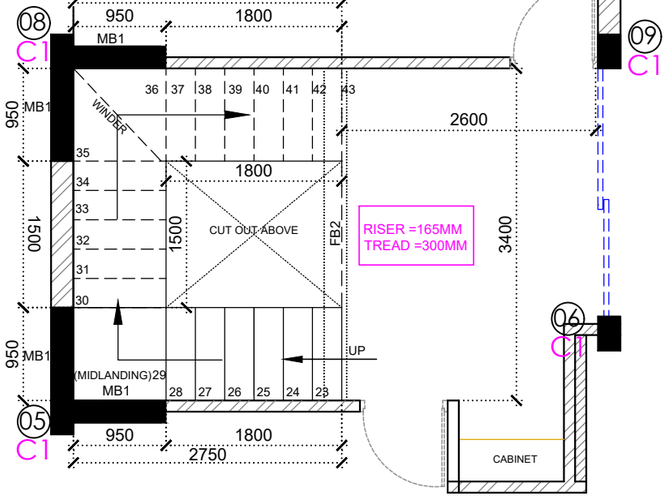

FIRST TO TERRACE FLOOR STAIRCASE PLAN

STUDIO ADROIT ARCHITECTS

ARCHITECTS # PLANNERS # INTERIOR DESIGNERS

AR.VAIBHAV THAKRE & AR. PRAJAKT KARMARKAR

Parijat Apartment,Flat 403, Plot no.M5,
West High Court Road, Laxmi Nagar, Nagpur, Maharashtra 440022

E-mail: studioadroitarchitects@gmail.com, ar.vaibhav.thakre@gmail.com Phone: 9167356380, 8552006111

SHEET TITLE
STAIRCASE DETAIL

PROJECT NO | DRAWING NO


BELONGS TO-
Dr. Umesh Thorat

DATE - 04/02/2023
DRAWN BY: PD | CHECKED

REVISIONS
REV 1
REV 2


N E W S

SCALE N.T.S

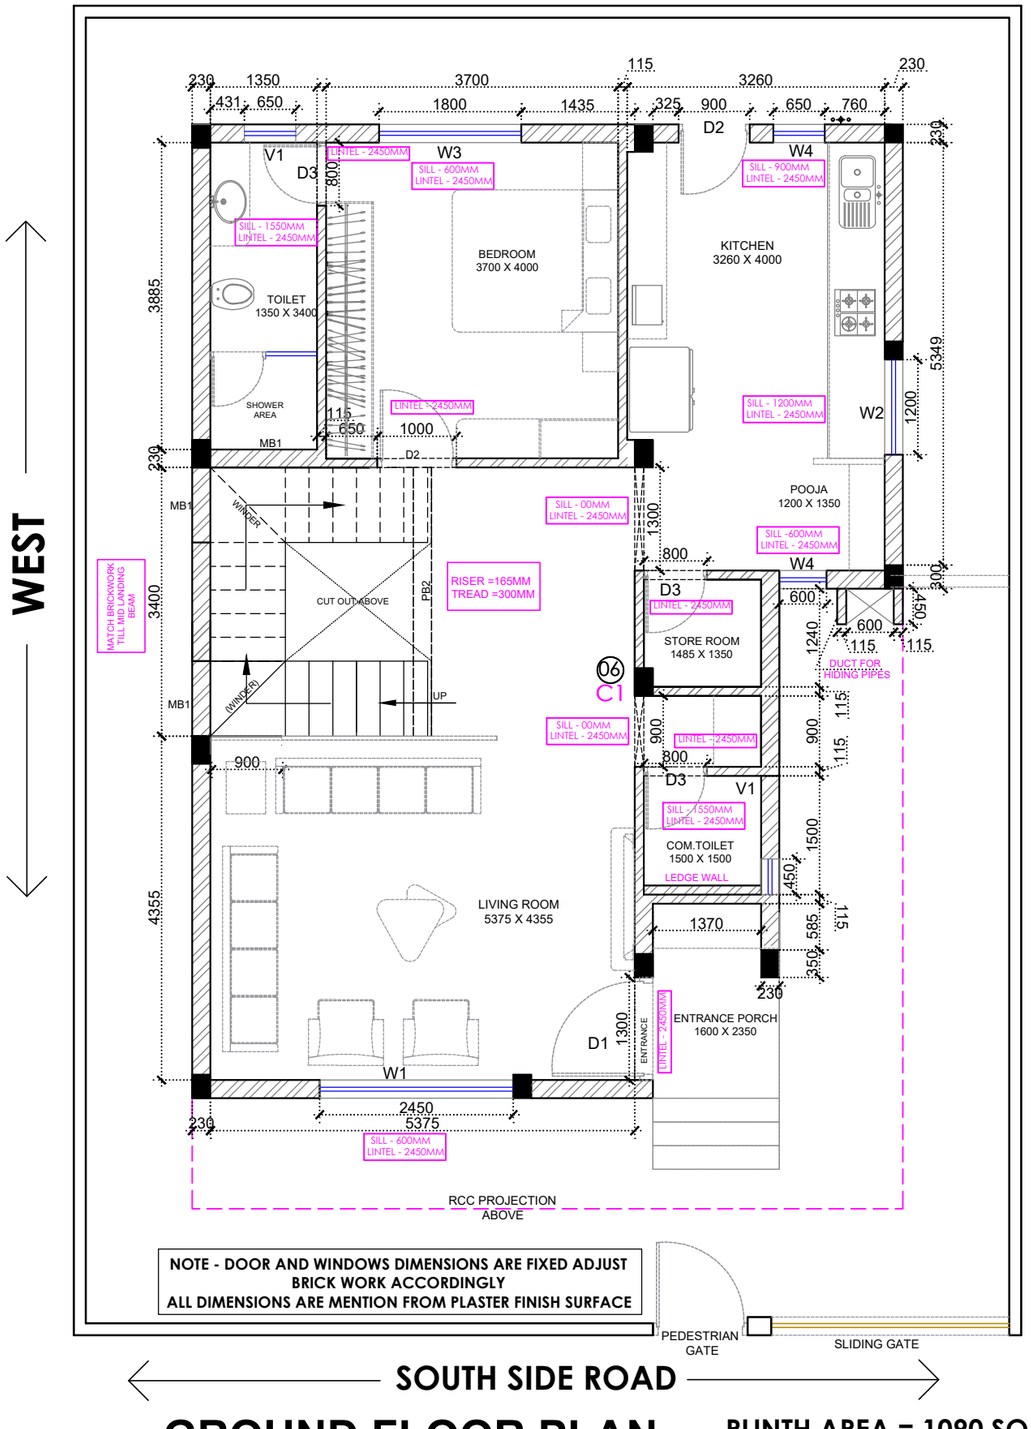

GROUND FLOOR PLAN

PLINTH AREA = 1090 SQ FT

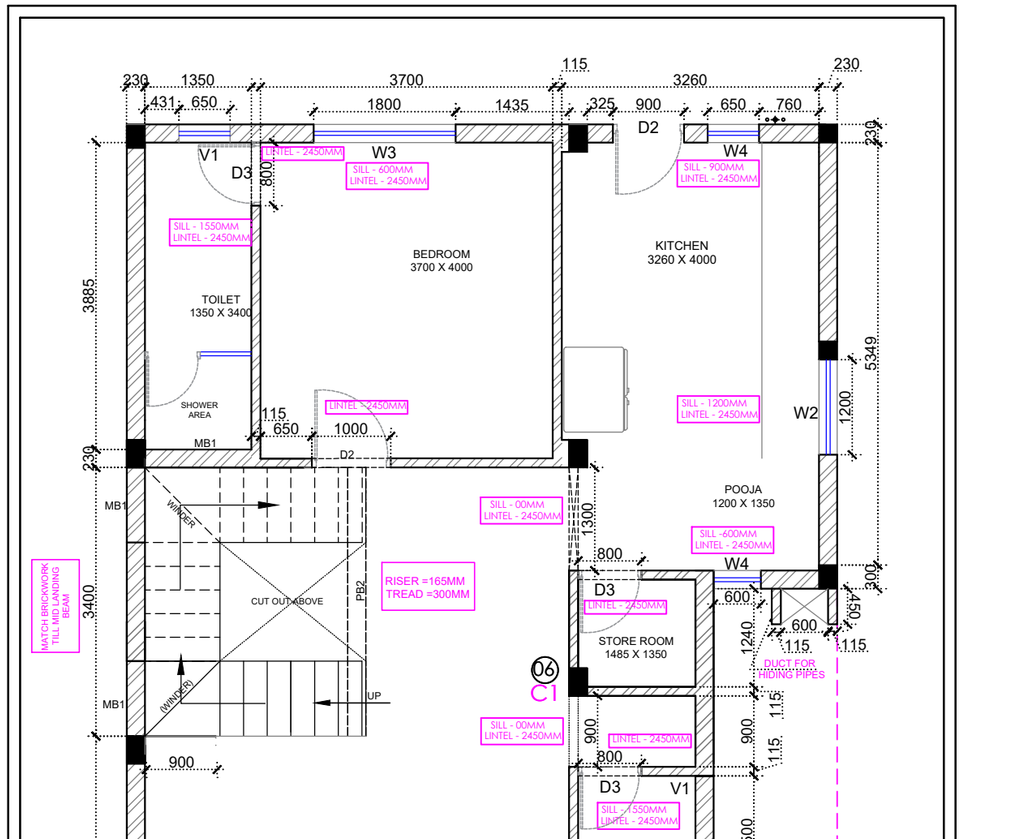

GROUND FLOOR PLAN

PLINTH AREA = 1090 SQ FT

STUDIO ADROIT ARCHITECTS

ARCHITECTS # PLANNERS # INTERIOR DESIGNERS

AR.VAIBHAV THAKRE & AR. PRAJAKT KARMARKAR

Parijat Apartment,Flat 403, Plot no.M5,
West High Court Road, Laxmi Nagar, Nagpur, Maharashtra 440022

E-mail: studioadroitarchitects@gmail.com, ar.vaibhav.thakre@gmail.com Phone: 9167356380, 8552006111

SHEET TITLE

BRICK WORK DRAWING

PROJECT NO | DRAWING NO

BELONGS TO-

Dr. Umesh Thorat

DATE - 25/02/2023

DRAWN BY: PD | CHECKED


REVISIONS

REV 1

REV 2

N E W S

SCALE N.T.S

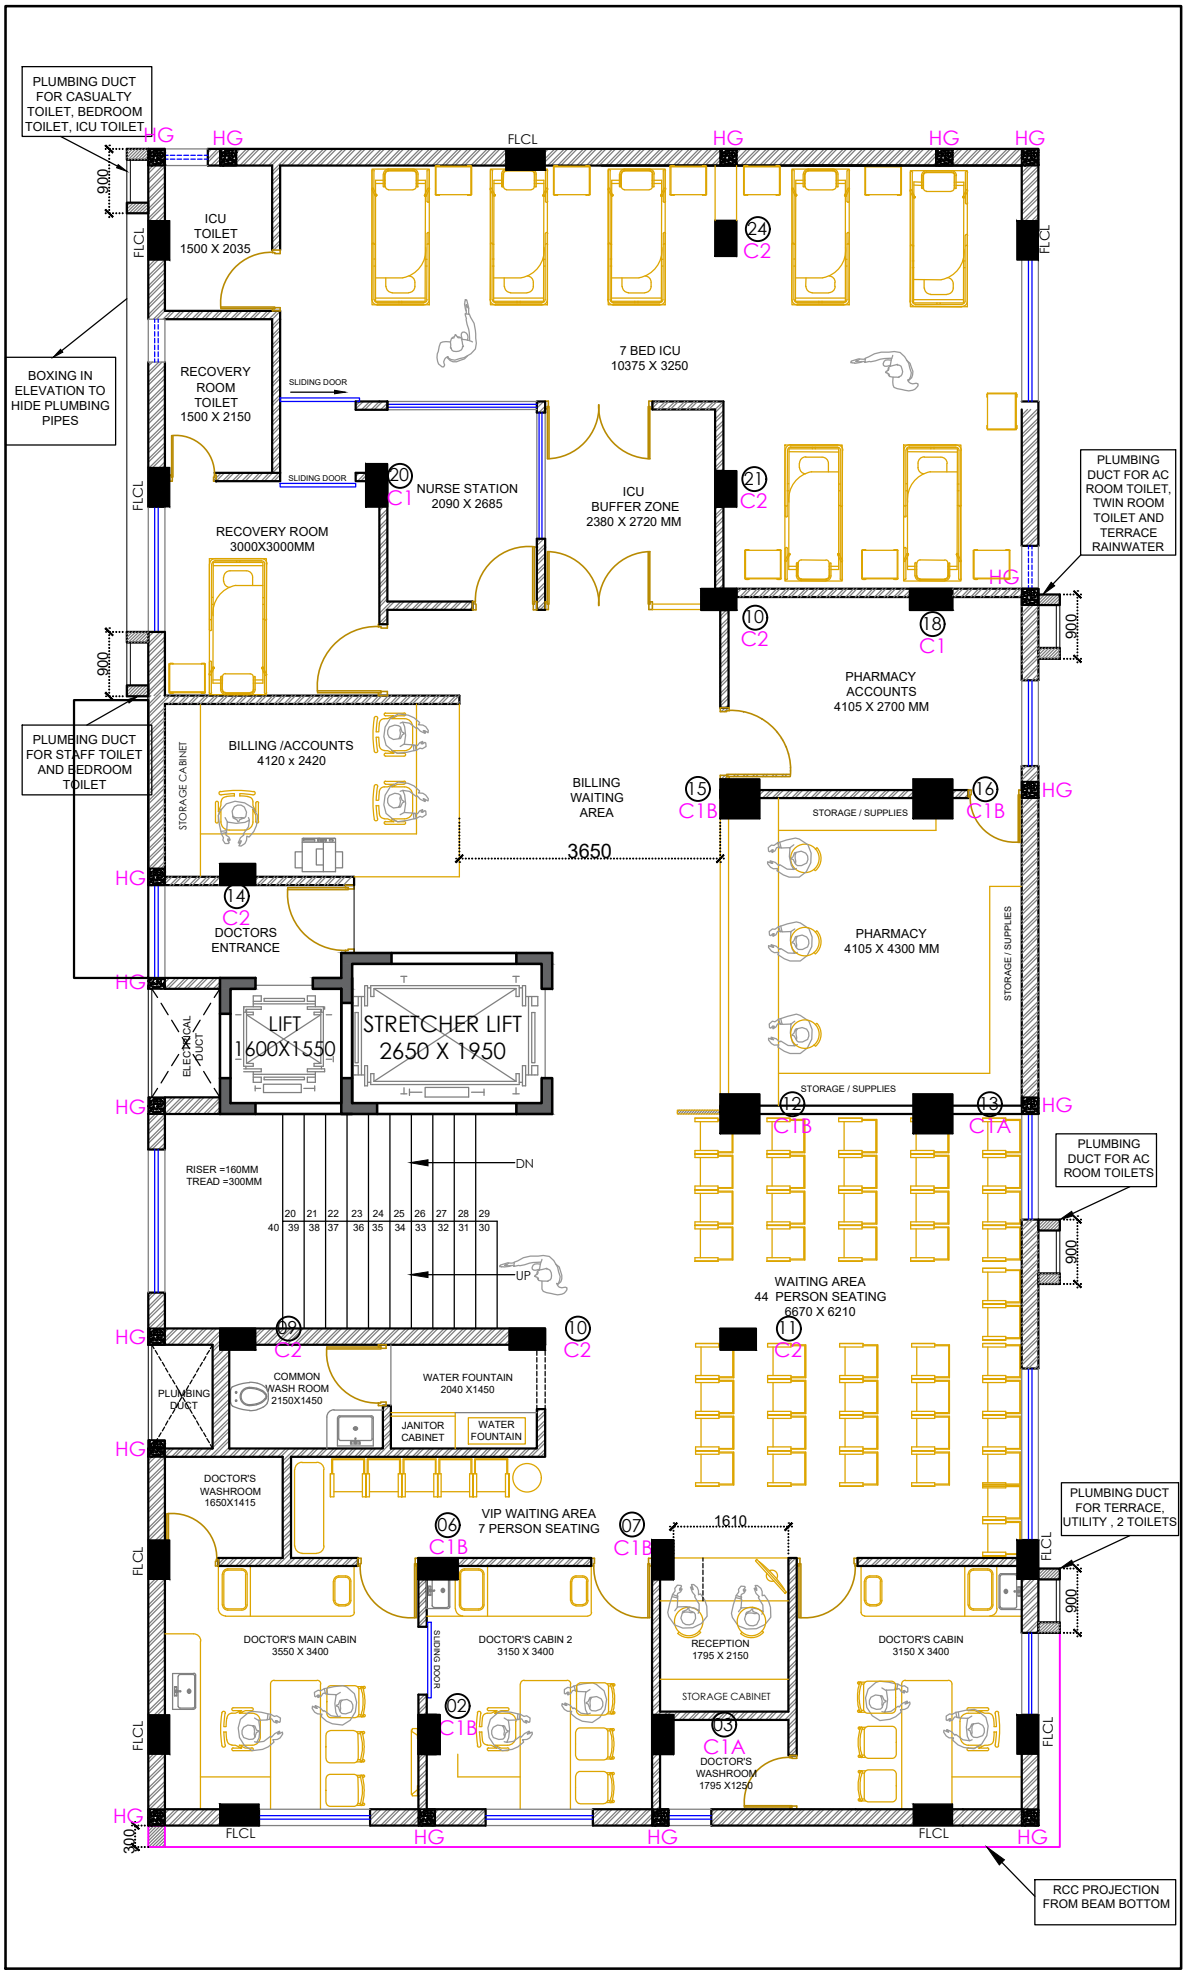

FIRST FLOOR PLAN

STUDIO ADROIT ARCHITECTS

ARCHITECTS # PLANNERS # INTERIOR DESIGNERS

AR.VAIBHAV THAKRE & AR. PRAJAKT KARMARKAR

Parijat Apartment,Flat 403, Plot no.M5,
West High Court Road, Laxmi Nagar, Nagpur, Maharashtra 440022

E-mail: studioadroitarchitects@gmail.com, ar.vaibhav.thakre@gmail.com Phone: 9167356380, 8552006111

SHEET TITLE
FIRST FLOOR PRESENTAION DRAWING

PROJECT NO | DRAWING NO


BELONGS TO-
Dr. Dahake

DATE - 11 FEB 2023
DRAWN BY:PD | CHECKED: PK

REVISIONS
REV 1
REV 2

N
W E
S

SCALE N.T.S

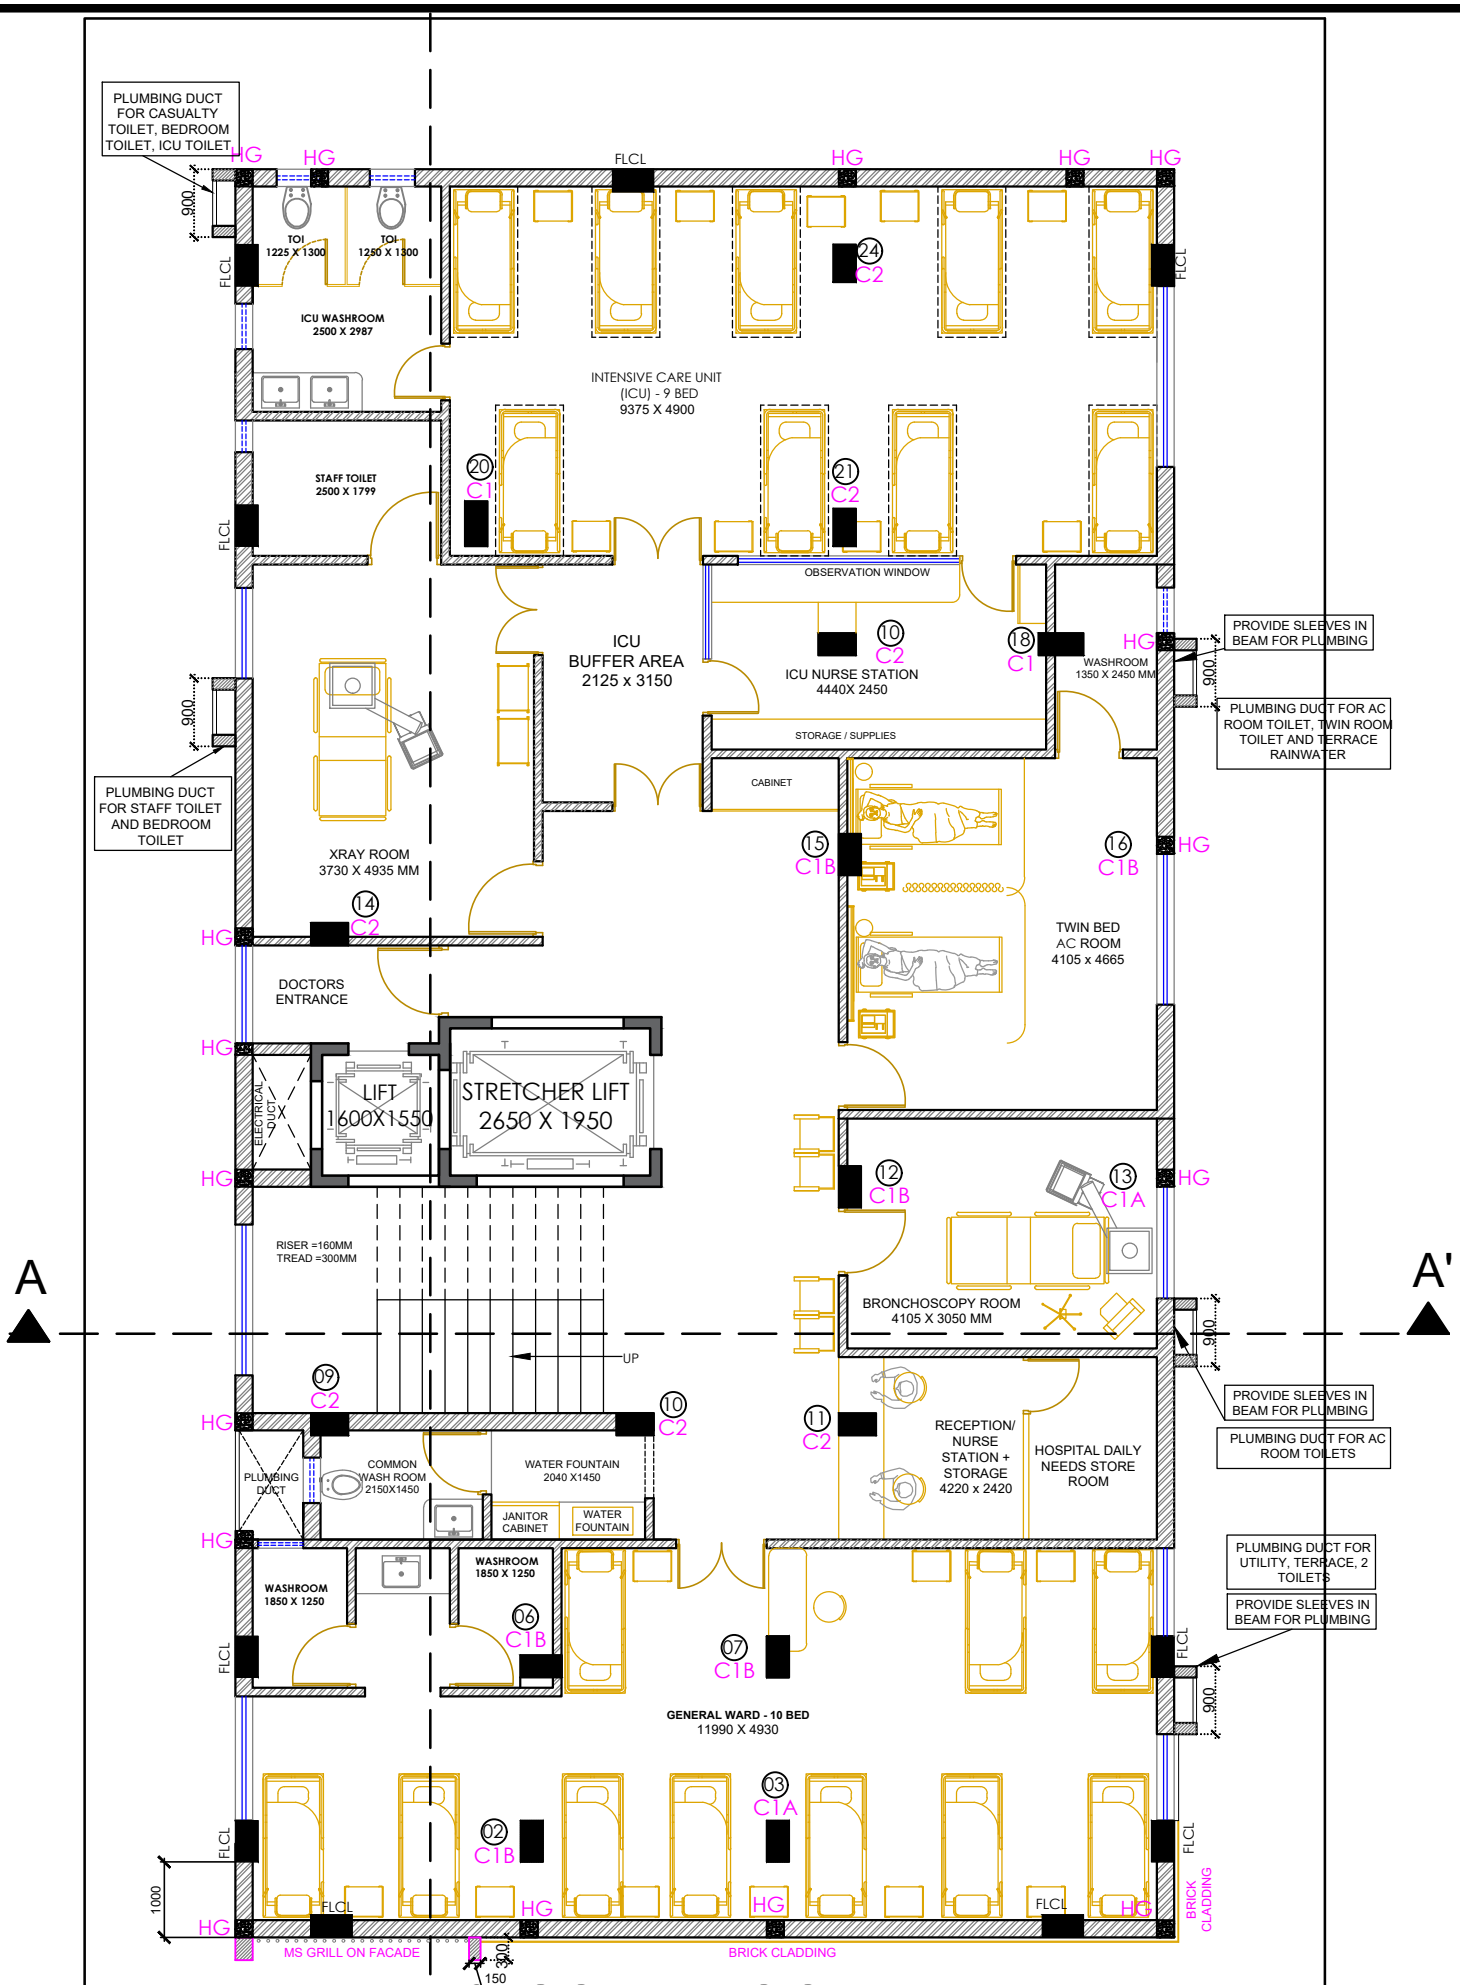

SECOND FLOOR PLAN

STUDIO ADROIT ARCHITECTS


ARCHITECTS # PLANNERS # INTERIOR DESIGNERS

AR.VAIBHAV THAKRE & AR. PRAJAKT KARMARKAR

Parijat Apartment,Flat 403, Plot no.M5,
West High Court Road, Laxmi Nagar, Nagpur, Maharashtra 440022

E-mail: studioadroitarchitects@gmail.com, ar.vaibhav.thakre@gmail.com Phone: 9167356380, 8552006111

SHEET TITLE **SECOND FLOOR PLAN**	BELONGS TO- **Dr. Dahake**	REVISIONS	N E S W
PROJECT NO / DRAWING NO	DATE - 20DEC 2022	REV 1	
	DRAWN BY:TS / CHECKED: PK	REV 2	SCALE N.T.S

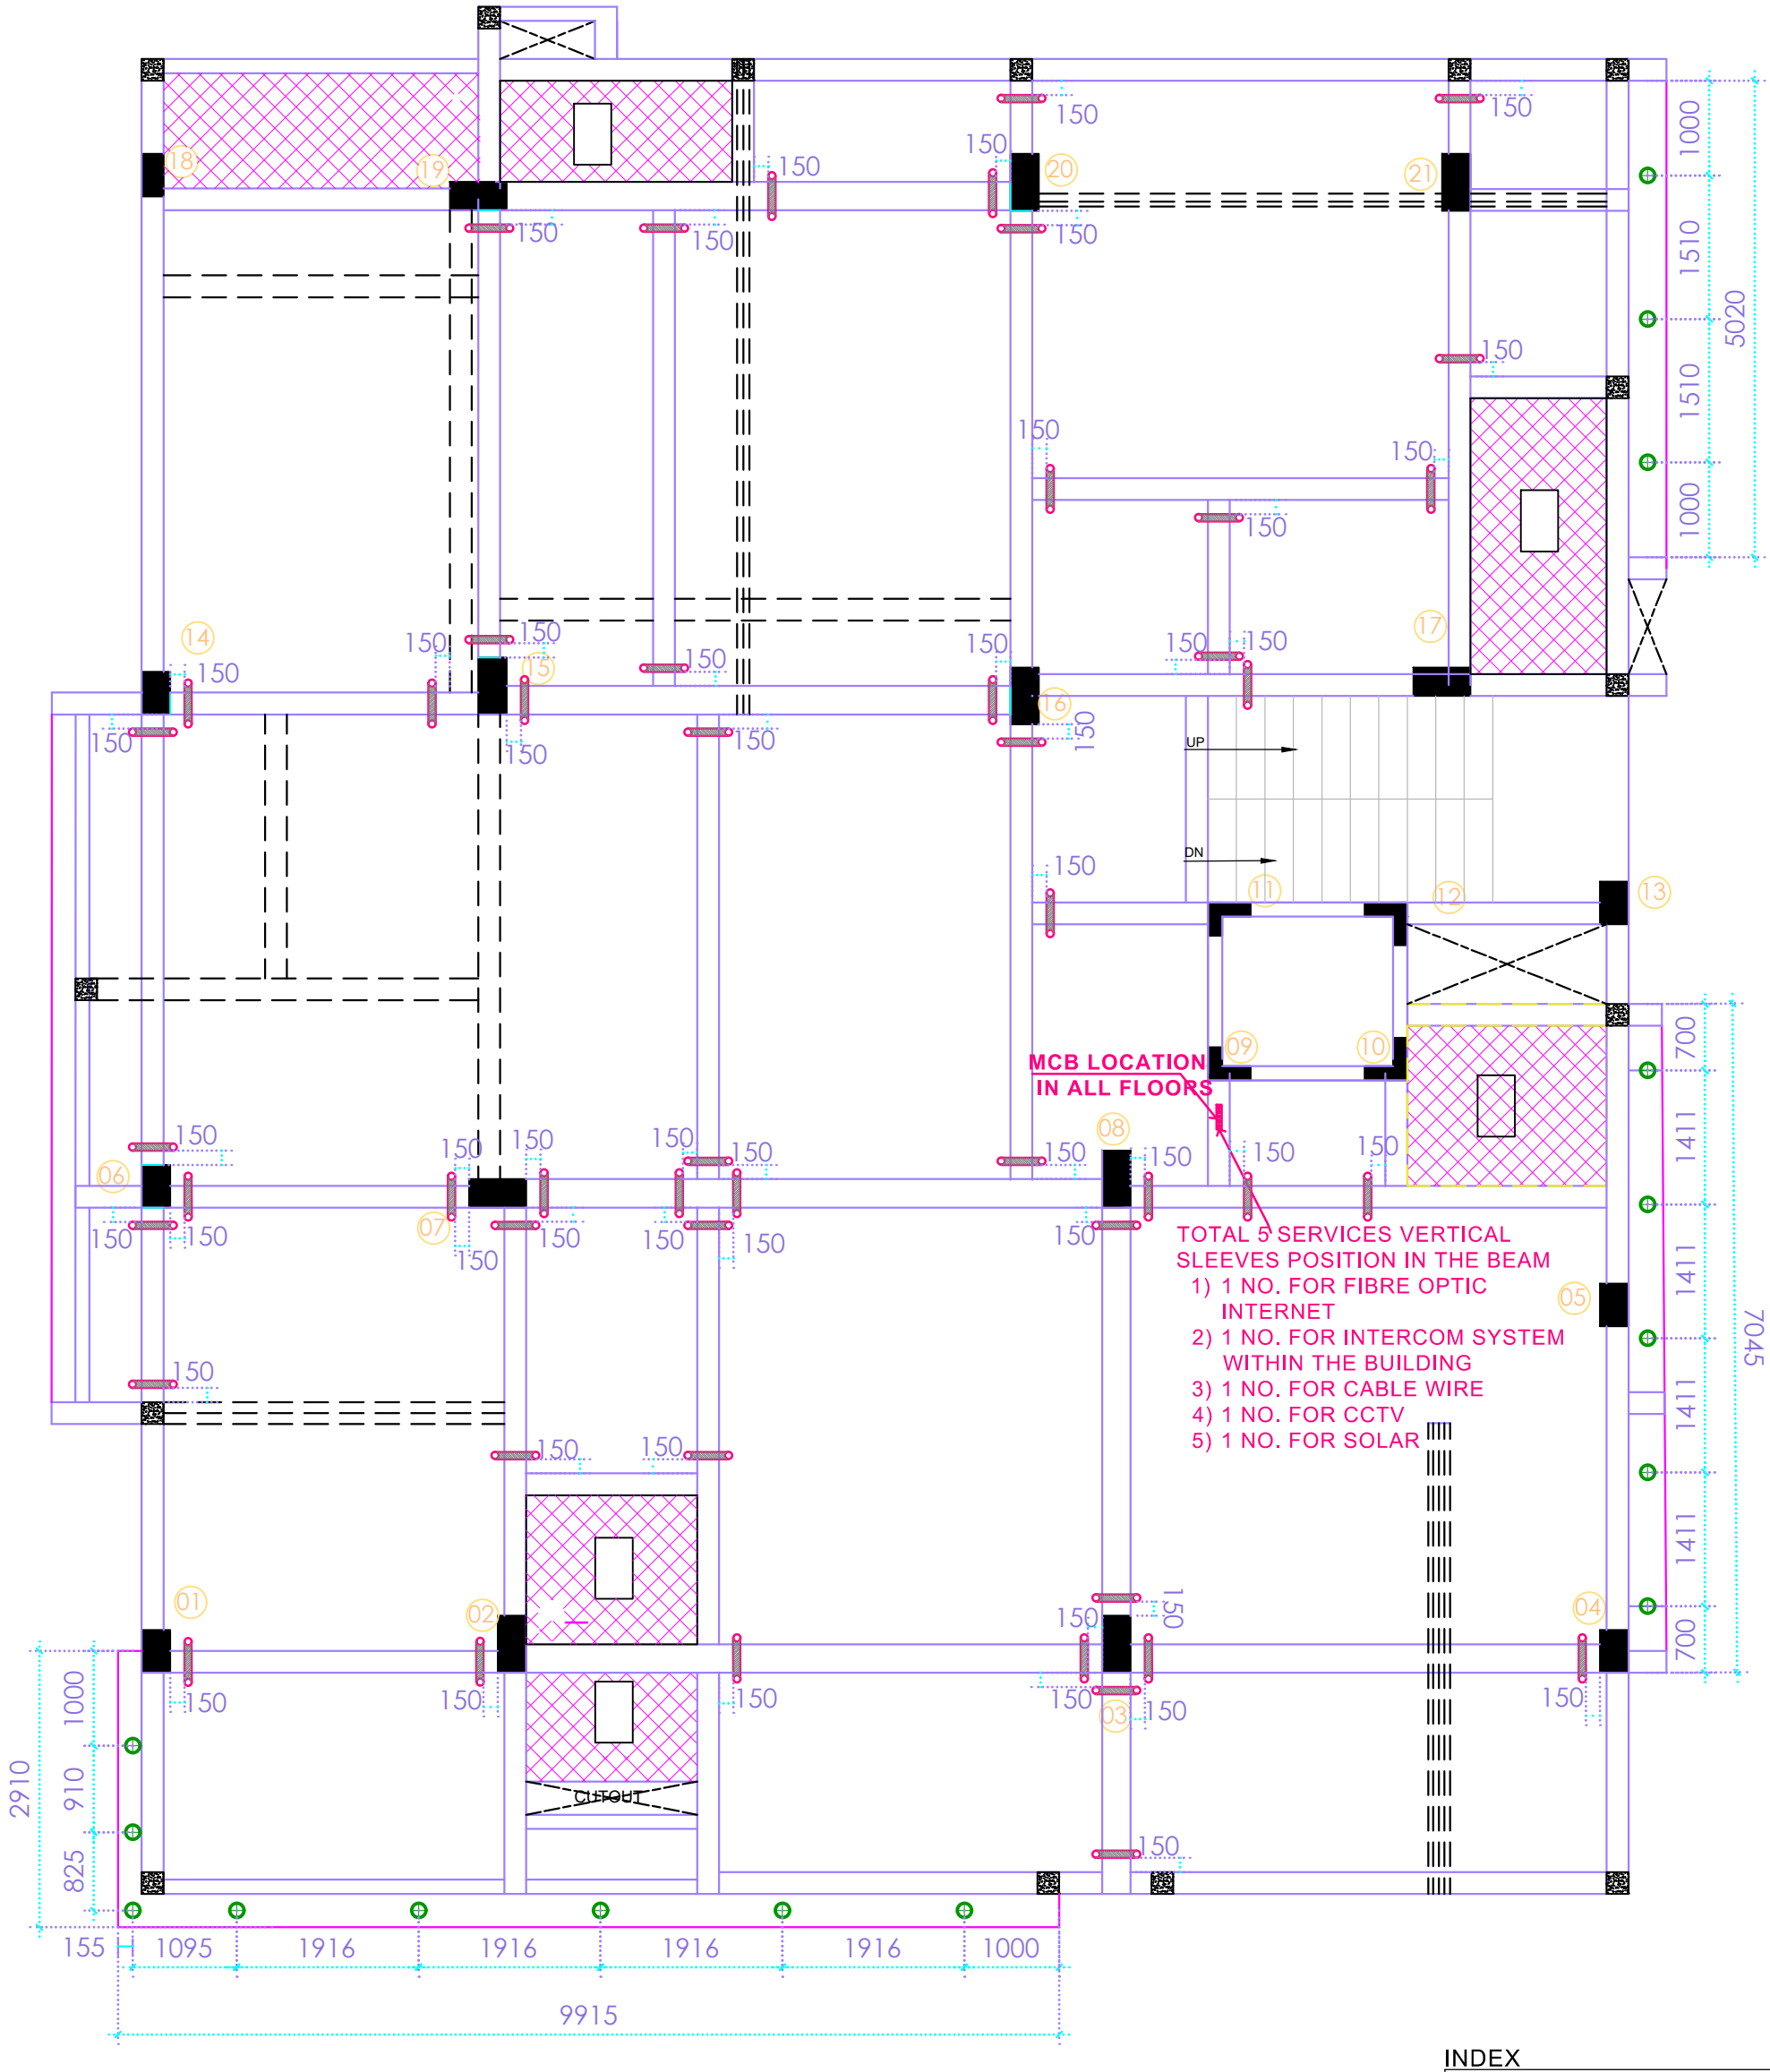

PLAN AT GROUND FLOOR ROOF SLAB

INDEX

- ELECTRICAL SLEEVES THROUGH BEAM (40MM)
- VERTICAL SLEEVES
- CEILING LIGHTS

STUDIO ADROIT ARCHITECTS

ARCHITECTS # PLANNERS # INTERIOR DESIGNERS

AR.VAIBHAV THAKRE & AR. PRAJAKT KARMARKAR

Parijat Apartment,Flat 403, Plot no.M5,
West High Court Road, Laxmi Nagar, Nagpur, Maharashtra 440022

E-mail: studioadroitarchitects@gmail.com, ar.vaibhav.thakre@gmail.com, Phone: 9167356380, 8552006111

SHEET TITLE	BELONGS TO-	REVISIONS	
ELECTRICAL SLEEVES	**KABRA RESIDENCE**		N
PROJECT NO / DRAWING NO	DATE - 25/02/2023	REV 1	E W S
	DRAWN BY:PD CHECKED:PK	REV 2	SCALE N.T.S





STUDIO ADROIT ARCHITECTS

ARCHITECTS # PLANNERS # INTERIOR DESIGNERS

AR.VAIBHAV THAKRE & AR. PRAJAKT KARMARKAR

Parijat Apartment,Flat 403, Plot no.M5,
West High Court Road, Laxmi Nagar, Nagpur, Maharashtra 440022

E-mail: studioadroitarchitects@gmail.com, ar.vaibhav.thakre@gmail.com Phone: 9167356380, 8552006111

SHEET TITLE

MUNDHADA RESIDENCE VIEWS

PROJECT NO

DRAWING NO

BELONGS TO-

MR. MUNDHADA

DATE - 23 02 2023

DRAWN BY: PD CHECKED VT

REVISIONS

REV 1

REV 2

S E W N

SCALE N.T.S